

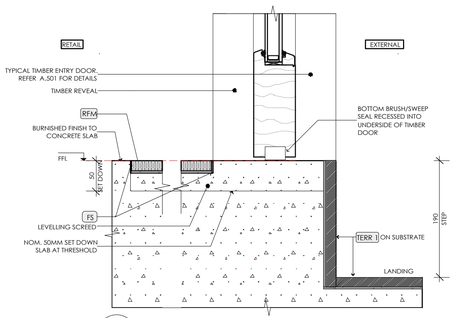



A RETAIL/ENTRY THRESHOLD
Scale: 1:5

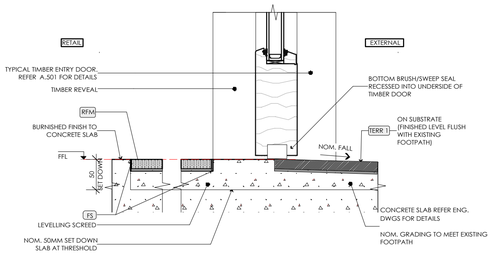


B RETAIL/ENTRY THRESHOLD
Scale: 1:5

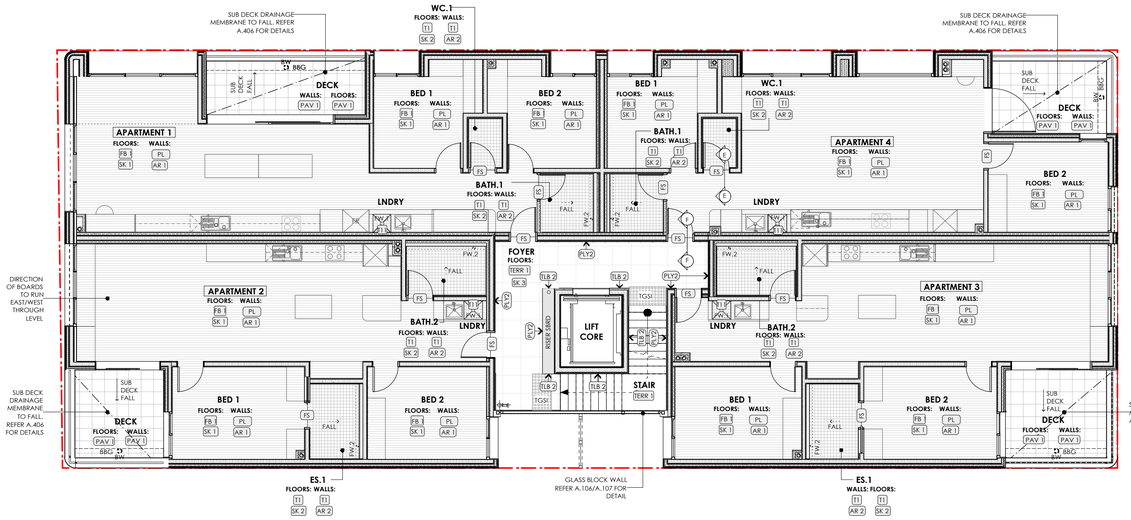


2 FINISHES PLAN - LEVEL 01
SCALE: 1:100

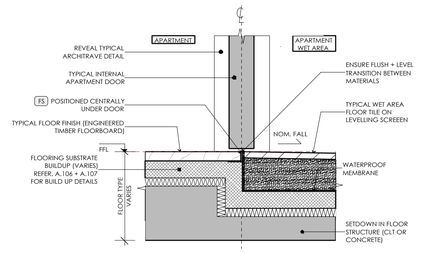


E TYPICAL APARTMENT WET AREA THREHSOLD
Scale: 1:5

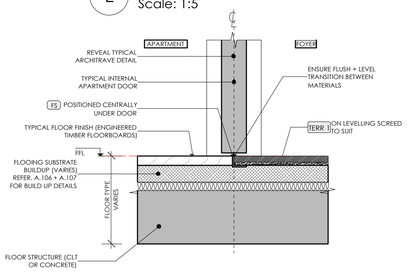


F TYPICAL APARTMENT/FOYER THREHSOLD
Scale: 1:5

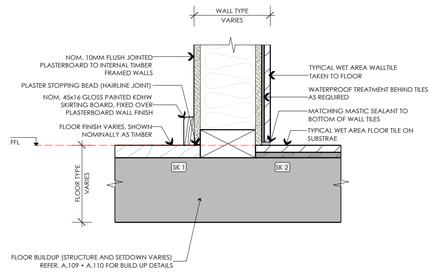


G SKIRTING TYPE 1 + 2
Scale: 1:5

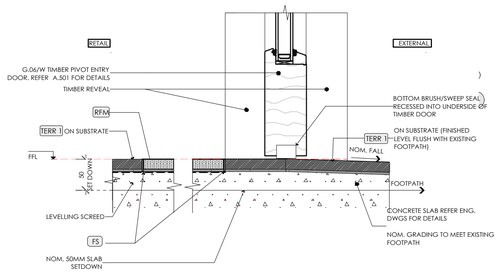


C FOYER/ENTRY THRESHOLD
Scale: 1:5

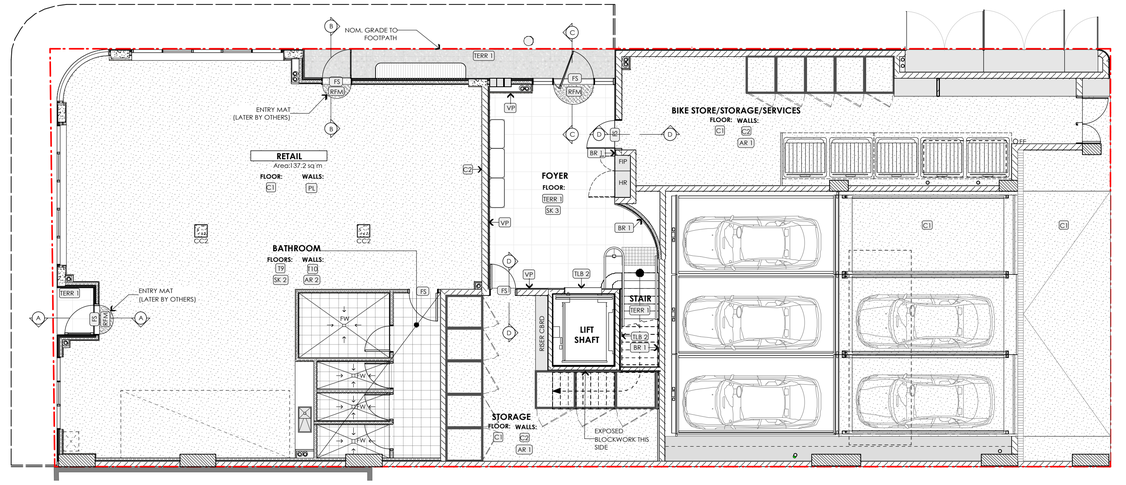


1 FINISHES PLAN - LEVEL GR
SCALE: 1:100

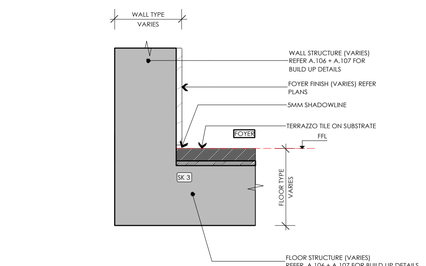

H SKIRTING TYPE 3
Scale: 1:5

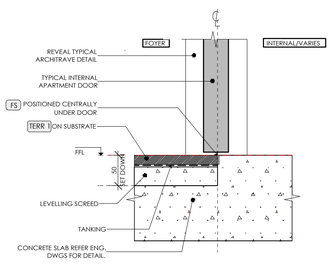

D FOYER THRESHOLD
Scale: 1:5

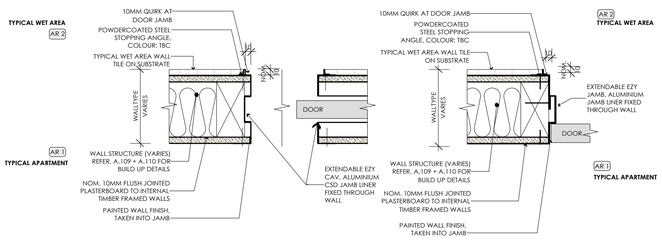

I TYPICAL ARCHITRAVE DETAILS
Scale: 1:5

FINISHES NOTES

- REFER TO SEPARATE INTERNAL FINISHES SCHEDULES FOR SPECIFIC SELECTIONS
- REFER TO FLOOR PLAN FOR FURTHER FLOOR FINISH DETAILS
- READ IN CONJUNCTION WITH PROJECT SPECIFICATION

SLIP RESISTANCE SCHEDULE

- AS PER BCA

FOYERS	P4
STAIRS	P4
PUBLIC CORRIDORS	P4
APARTMENT BATH/SHOWER	P4
RETAIL BATHROOMS	P4

REFER SCHEDULES FOR SELECTED PRODUCT INFORMATION

FINISHES LEGEND

GENERAL

FW 1	FLOOR WASTE 1	TILE INSET 1:100 FALL TO WASTE (REFER SCHEDULE FOR PRODUCT)
OUTLET SHOWN, NOM. FW.2	FLOOR WASTE 2 BATHROOM	STRIP DRAIN WITH TILE INSET LOCATE OUTLET ADJACENT SHOWER 1:100 FALL TO STRIP DRAIN (REFER SCHEDULE FOR PRODUCT)
BW	BALCONY WASTE	(REFER A.406 FOR DETAIL)
BBG	BALCONY SUB DECK BOX GUTTER	(REFER A.406 FOR DETAIL)
TGSI	TACTILE INDICATOR	(REFER SCHEDULE OF TACTILE INDICATORS FOR PRODUCT)

FLOOR FINISHES

C1	BURNISHED CONCRETE SLAB	
T1 > T11	SELECTED TILE	(REFER JOINERY DRAWINGS FOR SCOPE + SCHEDULES FOR TILE SELECTIONS)
TERR 1	SELECTED TERRAZZO STONE TILE	(REFER SCHEDULE OF FLOOR FINISHES FOR PRODUCT)
FB 1	SELECTED PREFINISHED ENGINEERED	(REFER SCHEDULE OF FLOOR FINISHES FOR PRODUCT)
FB 2	SELECTED PREFINISHED ENGINEERED	(REFER SCHEDULE OF FLOOR FINISHES FOR PRODUCT)
T12	SELECTED TIMBER DECKING	(REFER SCHEDULE OF FLOOR FINISHES FOR PRODUCT)
PAV 1	SELECTED TERACOTTA TILE	(REFER SCHEDULE OF FLOOR FINISHES FOR PRODUCT)
MG	SELECTED METAL GRATE	(REFER A.106/A.107 FOR DETAILS)
RFM	SELECTED RECESSED FLOOR MAT	(REFER SCHEDULE OF FLOOR FINISHES FOR PRODUCT)
FS	FLOOR STRIP	STEEL FLAT BAR RECESSED INTO FLOOR POWDERCOATED BLACK

FLOOR SUBSTRATES

CONC	CONCRETE (STRUCTURAL SUBSTRATE)	

WALLS FINISHES

T1 > T11	SELECTED TILE	(REFER JOINERY DRAWINGS FOR SCOPE + SCHEDULES FOR TILE SELECTIONS)
E2	STRUCTURAL CONCRETE BLOCK	(REFER A.106/A.107 FOR DETAILS + SCHEDULES FOR PAINT COLOURS)
PL	WALL WITH PLASTER + PAINT FINISH	(REFER A.106/A.107 FOR DETAILS + SCHEDULES FOR PAINT COLOURS)
VP	VITRAPANEL	(REFER JOINERY DRAWINGS FOR SCOPE + REFER A.106/A.107 FOR DETAIL)
PAV 1	TERRACOTTA TILE	(REFER A.106/A.107 FOR DETAILS + SCHEDULES FOR PRODUCT)
TLB 2	INTERNAL TIMBER LINING	(REFER SCHEDULES FOR PRODUCT)
PLY2	PLYWOOD SHEET	(REFER SCHEDULE FOR PRODUCT DETAIL)
BR 1	EXTERNAL BRICK CLADDING	(REFER A.106/A.107 FOR DETAIL)

ARCHITRAVES

AR 1	ARCHITRAVE TYPE 1 PRODUCT: EZY JAMB	- GENERAL (REFER TO TYPICAL SQUARE SET JAMB DETAIL)
AR 2	ARCHITRAVE TYPE 2 PRODUCT: EZY JAMB	- TILED (REFER TO TYPICAL TILED JAMB DETAIL)

SKIRTINGS

SK 1	SKIRTING TYPE 1	- GENERAL APARTMENT (REFER A.206 FOR TYPICAL DETAIL)
SK 2	SKIRTING TYPE 2	- WET AREA TILED (REFER A.206 FOR TYPICAL DETAIL)
SK 3	SKIRTING TYPE 3	- FOYER SKIRTING (REFER A.206 FOR TYPICAL DETAIL)

This drawing to read in conjunction with the project specification and any instructions issued during the course of the contract. Do not scale any dimension from drawing. Refer to architect of all discrepancies in document.

ISSUE	DATE	REVISION
D	17/12/19	FOR CONSTRUCTION
C	31/5/19	CONTRACT SET

FOR CONSTRUCTION - 17/12/19

CLIENT H.CHARALAMBOUS
Gardiner Architects
7/252 St Georges Rd, Fitzroy North, VIC, 3068
Ph: (03) 9486 4092 E: info@paulgardiner.com.au

DWG FINISHES PLAN - BASEMENT + GROUND FLOOR
PROJECT RETAIL/RESIDENTIAL DEVELOPMENT 752 HIGH STREET, THORNBURY
DRAWN BY AM
SCALE 1:100 @ A1
JOB NO 141211
A.206
DWG # REV# D