




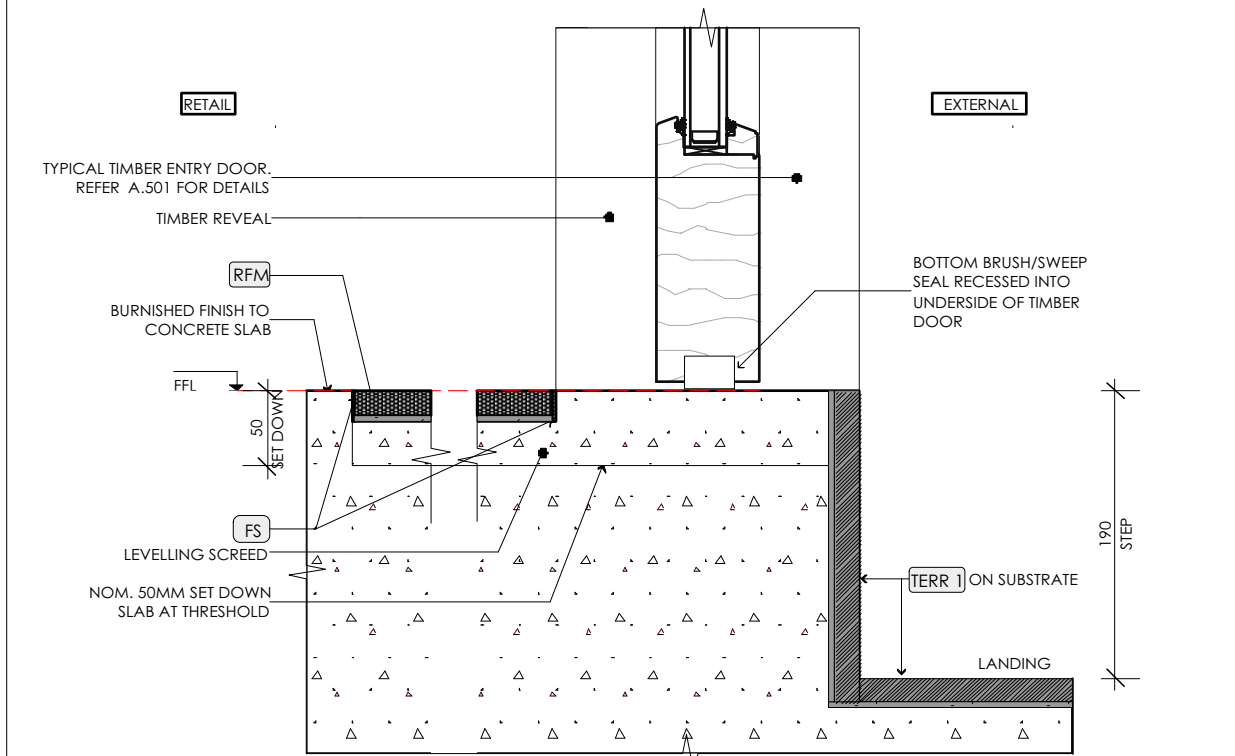


A RETAIL/ENTRY THRESHOLD
Scale: 1:5

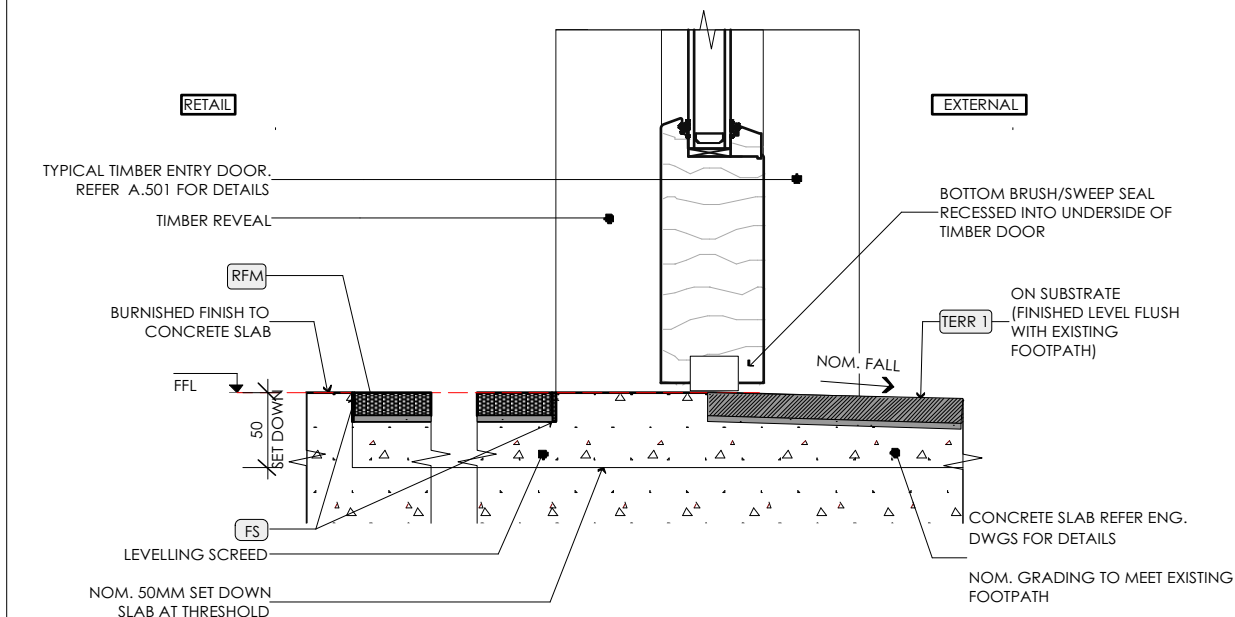


B RETAIL/ENTRY THRESHOLD
Scale: 1:5

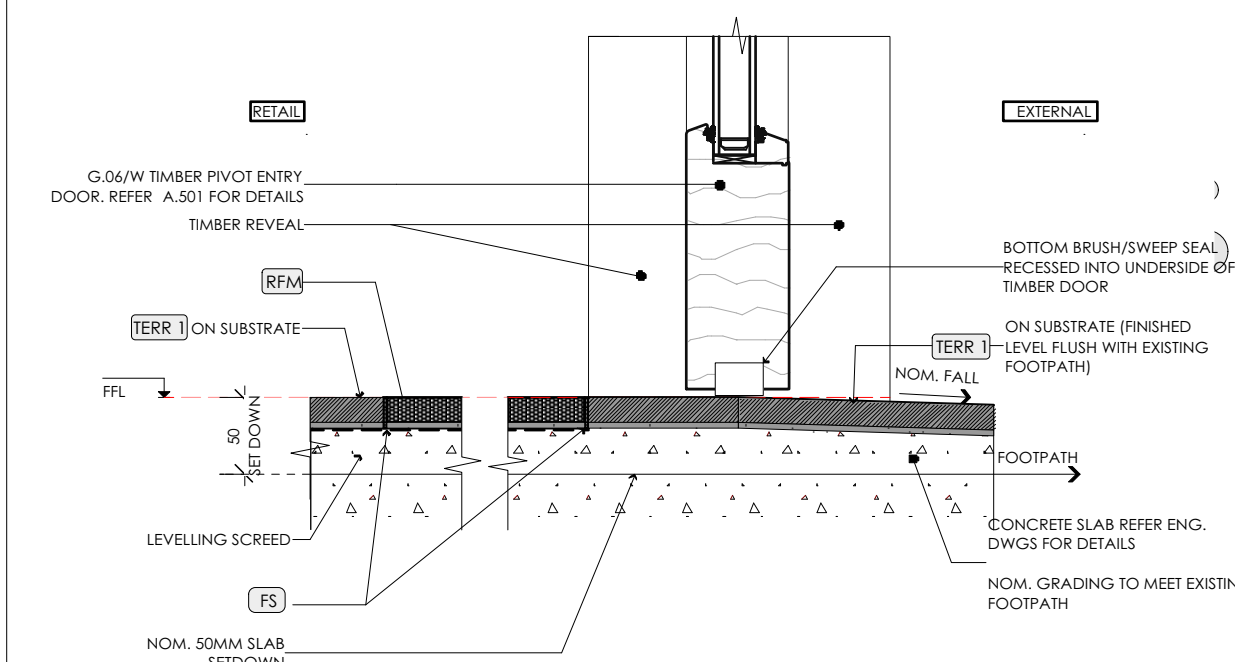


C FOYER/ENTRY THRESHOLD
Scale: 1:5

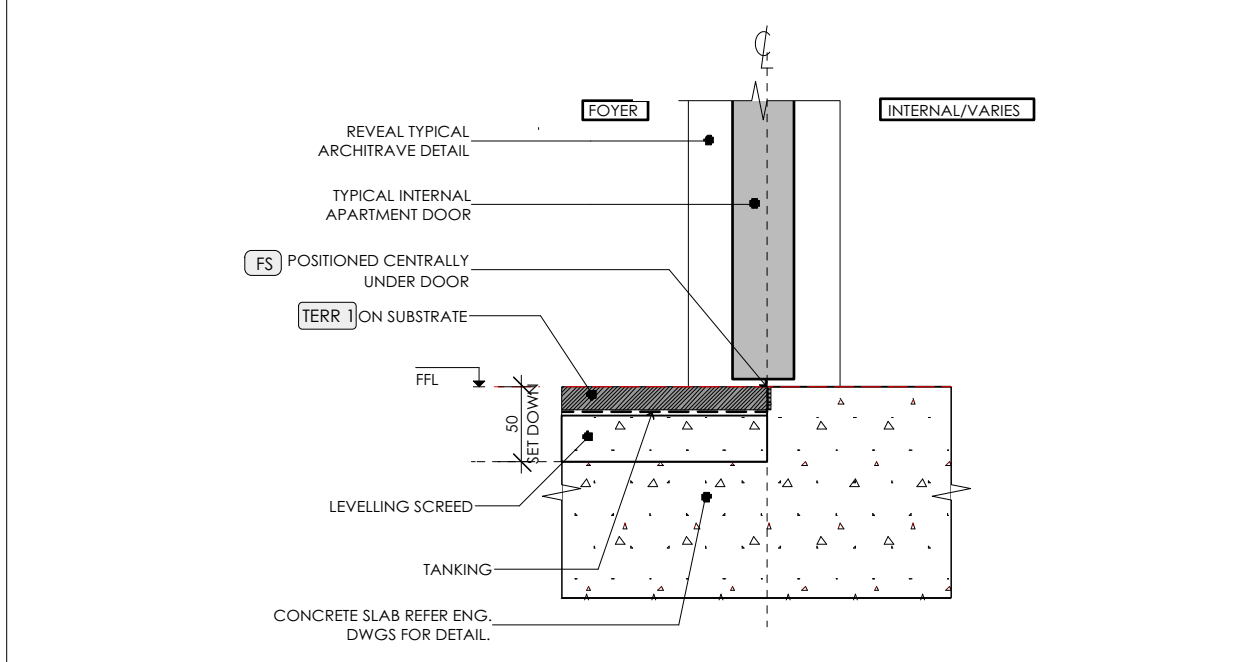


D FOYER THRESHOLD
Scale: 1:5

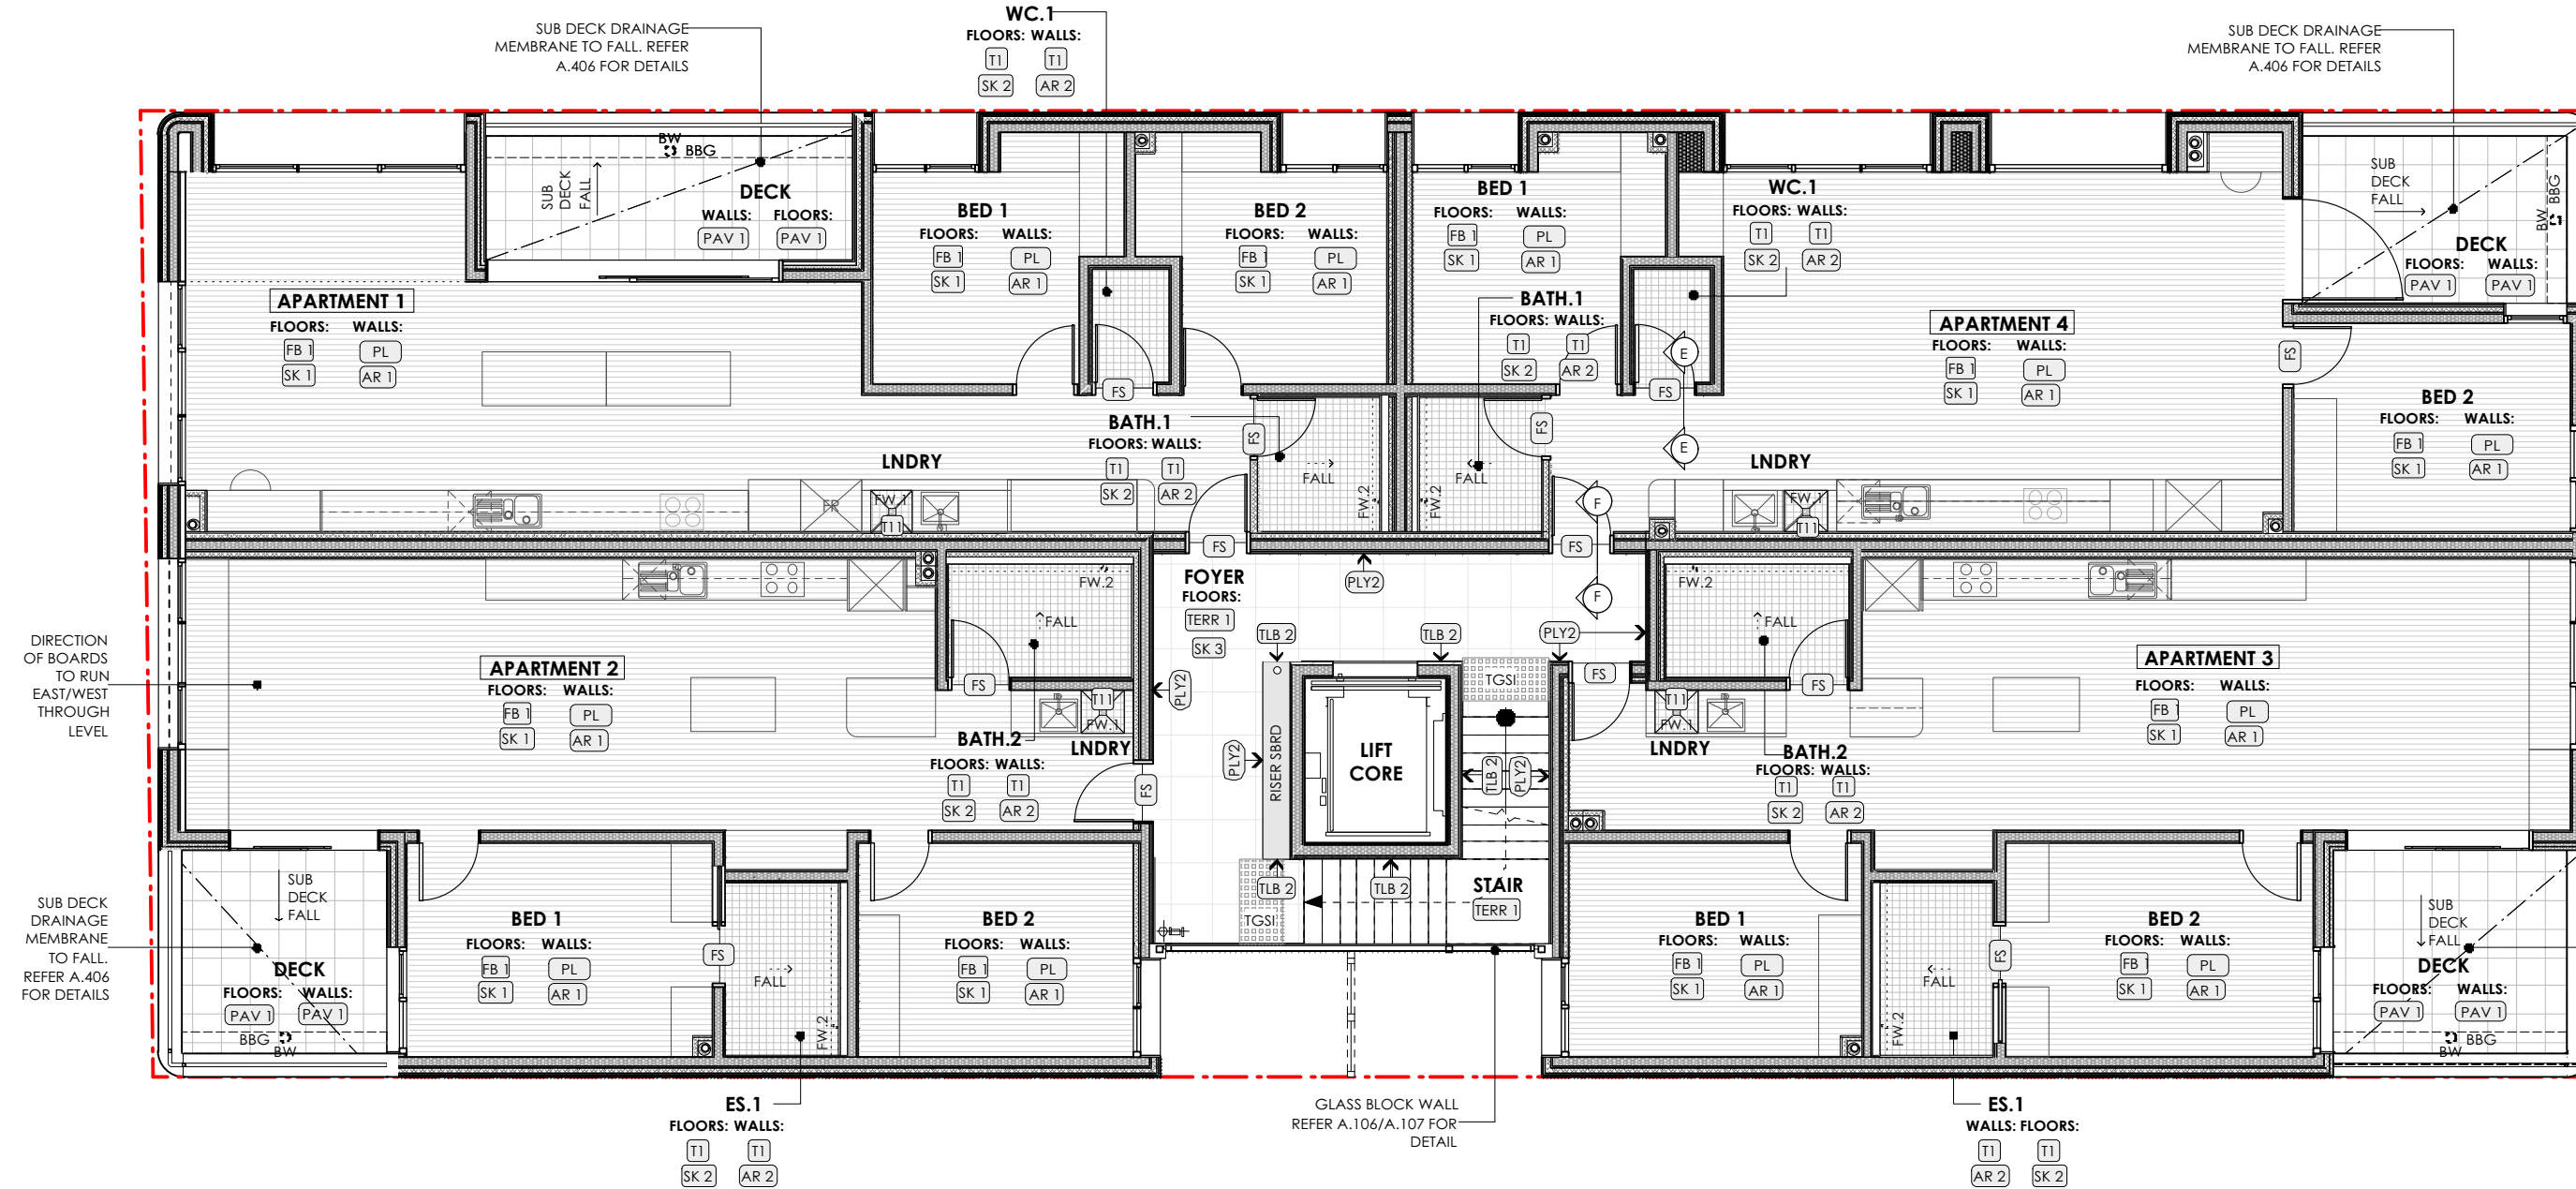


2 FINISHES PLAN - LEVEL 01
SCALE: 1:100

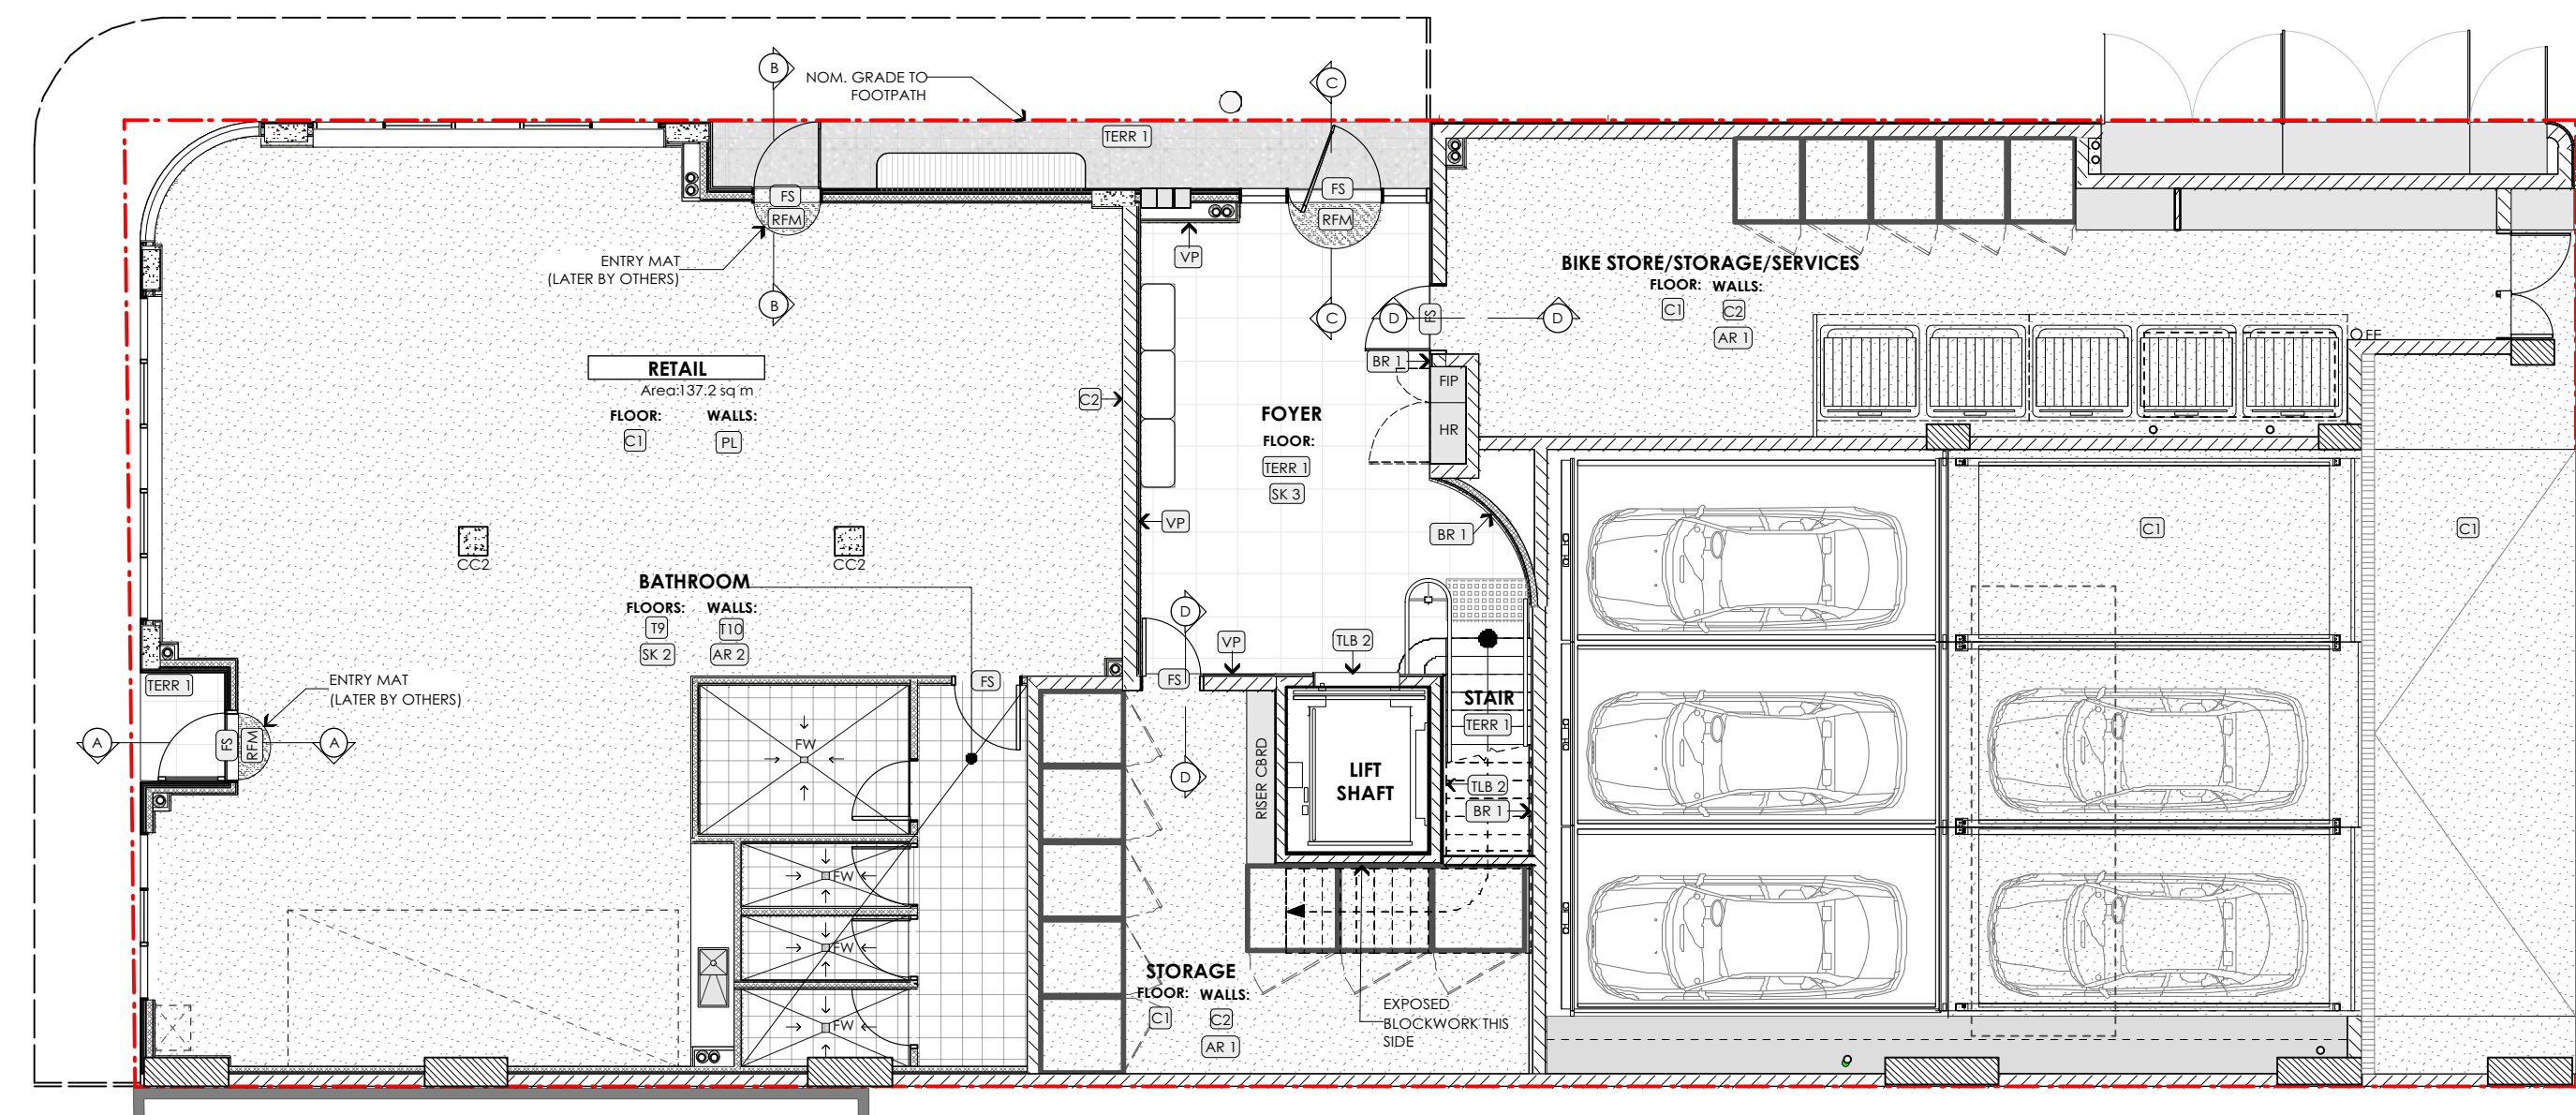


1 FINISHES PLAN - LEVEL GR
SCALE: 1:100

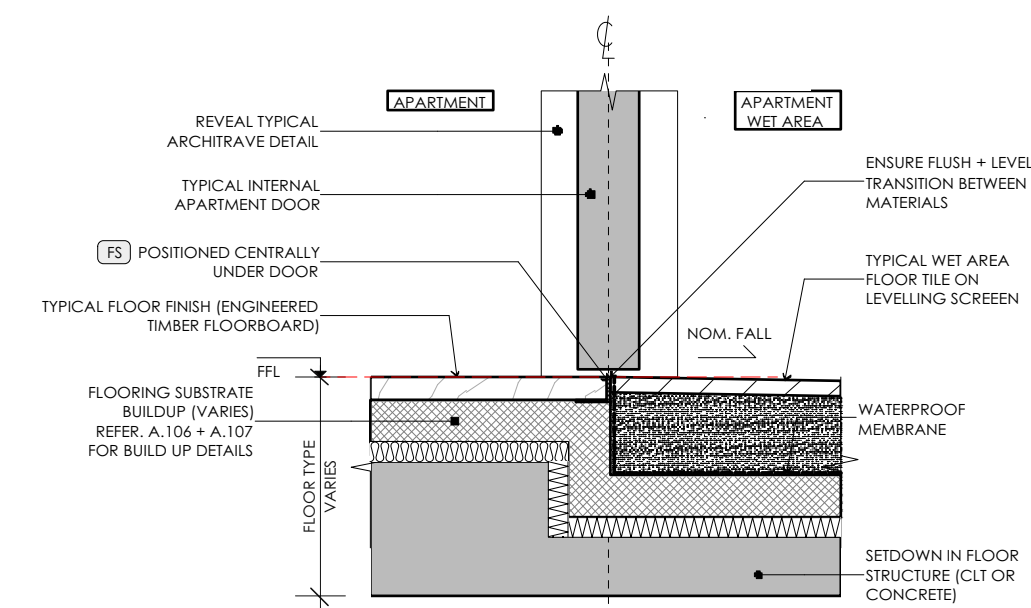


E TYPICAL APARTMENT WET AREA THRESHOLD
Scale: 1:5

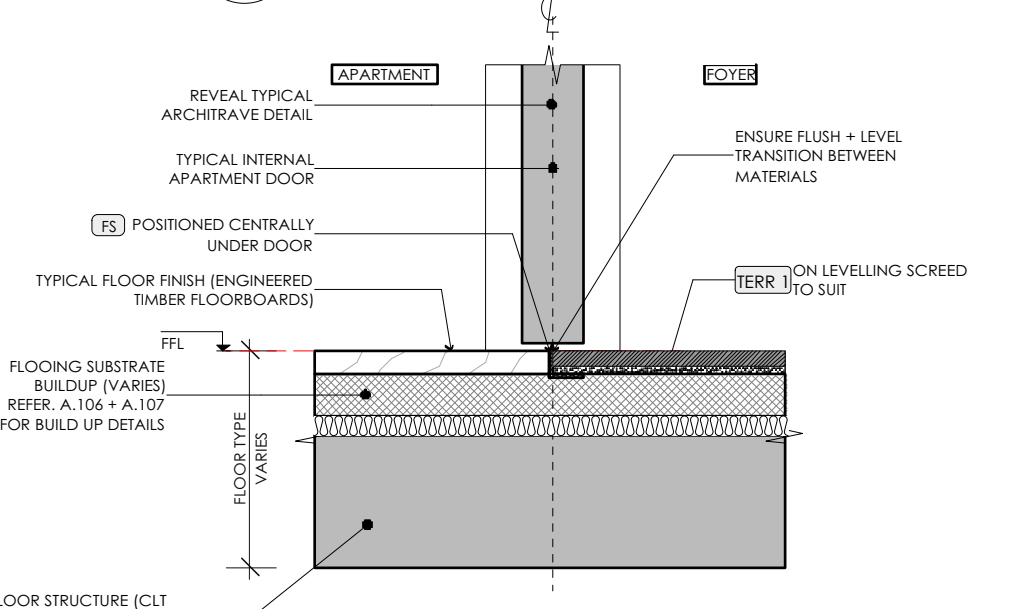


F TYPICAL APARTMENT/FOYER THRESHOLD
Scale: 1:5

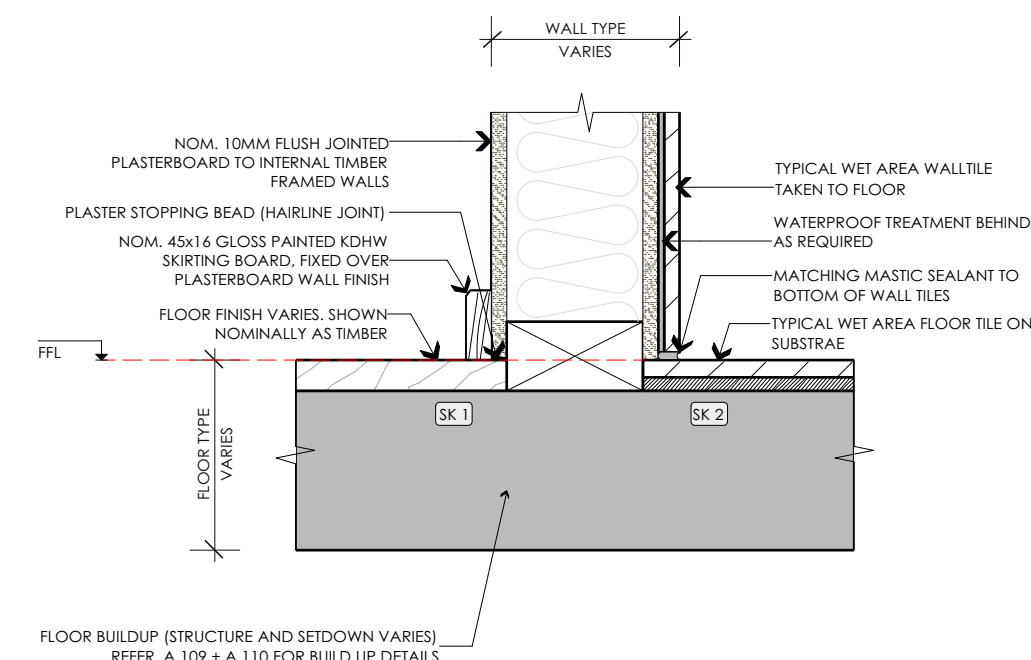

G SKIRTING TYPE 1 + 2
Scale: 1:5

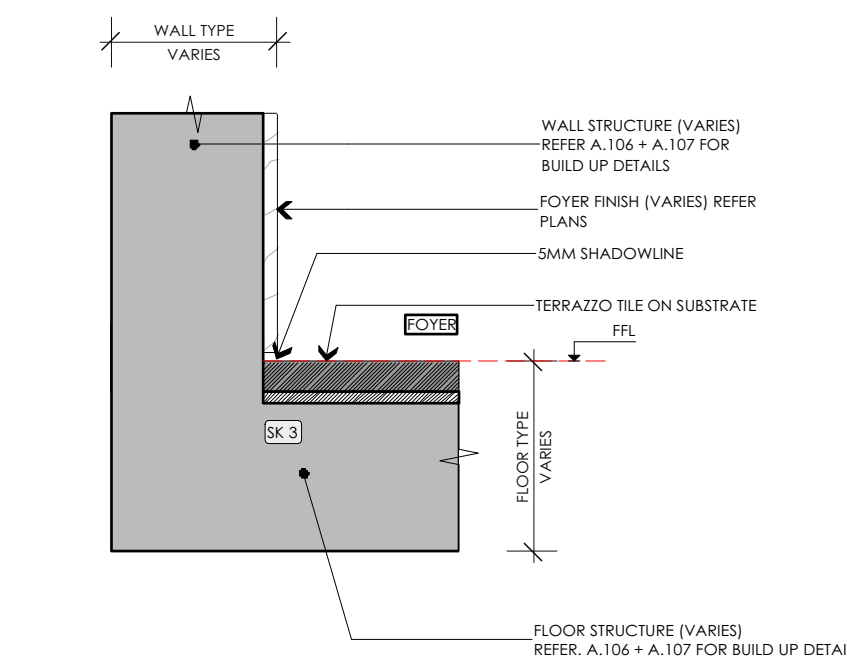

H SKIRTING TYPE 3
Scale: 1:5

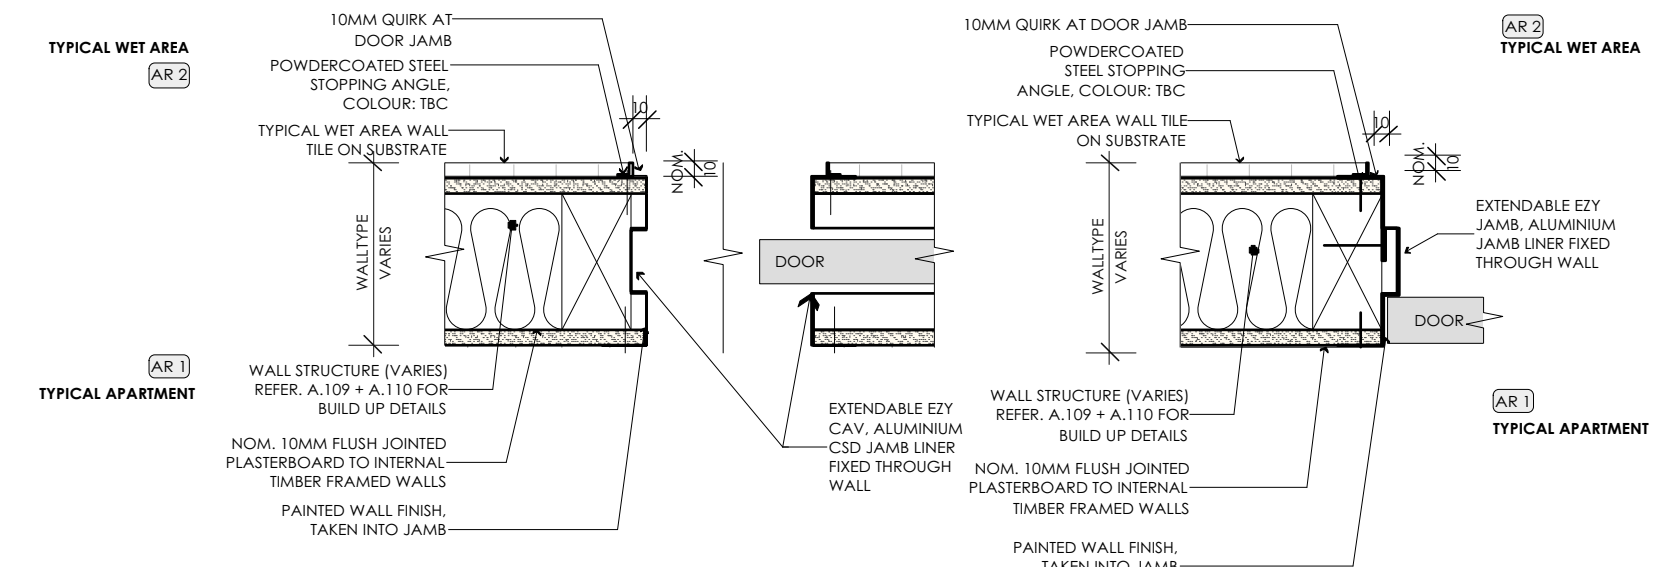

I TYPICAL ARCHITRAVE DETAILS
Scale: 1:5

FINISHES NOTES	
- REFER TO SEPARATE INTERNAL FINISHES SCHEDULES FOR SPECIFIC SELECTIONS	
- REFER TO FLOOR PLAN FOR FURTHER FLOOR FINISH DETAILS	
- READ IN CONJUNCTION WITH PROJECT SPECIFICATION	

SLIP RESISTANCE SCHEDULE	
- AS PER BCA	
FOYERS	P4
STAIRS	P4
PUBLIC CORRIDORS	P4
APARTMENT BATH/SHOWER	P4
RETAIL BATHROOMS	P4

REFER SCHEDULES FOR SELECTED PRODUCT INFORMATION	

FINISHES LEGEND	
GENERAL	
FW.1	FLOOR WASTE 1
FW.2	FLOOR WASTE 2
BW	BALCONY WASTE
BBG	BALCONY SUB DECK BOX GUTTER
TGSI	TACTILE INDICATOR
TILE INSET	1:100 FALL TO WASTE (REFER SCHEDULE FOR PRODUCT)
STRIP DRAIN WITH TILE INSET	LOCATE OUTLET ADJACENT SHOWER (REFER SCHEDULE FOR PRODUCT)
1:100 FALL TO STRIP DRAIN	(REFER SCHEDULE FOR PRODUCT)
REFER A.406 FOR DETAILS	
REFER A.406 FOR DETAILS	
REFER SCHEDULE OF TACTILE INDICATORS FOR PRODUCT	

FLOOR FINISHES	
CL	BURNISHED CONCRETE SLAB
TT	SELECTED TILE
TERR	SELECTED TERRAZZO STONE TILE
PE	SELECTED PREFINISHED ENGINEERED
PEB	SELECTED PREFINISHED ENGINEERED
TD	SELECTED TIMBER DECKING
PAV.1	SELECTED TERRAZZO TILE
MG	SELECTED METAL GRATE
RFM	SELECTED RECESSED FLOOR MAT
FS	FLOOR STRIP
	STEEL FLAT BAR RECESSED INTO FLOOR POWDERCOATED BLACK

FLOOR SUBSTRATES	
CONC	CONCRETE (STRUCTURAL SUBSTRATE)

WALLS FINISHES	
TT	SELECTED TILE
SC	STRUCTURAL CONCRETE BLOCK
W	WALL WITH PLASTER + PAINT FINISH
VP	VITRAPANEL
PAV.1	TERRAZZO TILE
TLB.2	INTERNAL TIMBER LINING
PLYV	PLYWOOD SHEET
BR.1	EXTERNAL BRICK CLADDING
	(REFER JONERY DRAWINGS FOR SCOPE + SCHEDULES FOR TILE SELECTIONS)
	(REFER A.106/A.107 FOR DETAILS + SCHEDULES FOR PAINT COLOURS)
	(REFER JONERY DRAWINGS FOR SCOPE + REFER A.106/A.107 FOR DETAILS)
	(REFER A.106/A.107 FOR DETAILS + SCHEDULES FOR PAINT COLOURS)
	(REFER JONERY DRAWINGS FOR SCOPE + REFER A.106/A.107 FOR DETAILS)
	(REFER SCHEDULES FOR PRODUCT)
	(REFER SCHEDULE FOR PRODUCT DETAILS)
	(REFER A.106/A.107 FOR DETAILS)

ARCHITRAVES	
AR.1	ARCHITRAVE TYPE 1
AR.2	ARCHITRAVE TYPE 2
	(REFER TO TYPICAL SQUARE SET JAMB DETAILS)
	(REFER TO TYPICAL TILED JAMB DETAILS)

SKIRTINGS	
SK.1	SKIRTING TYPE 1
SK.2	SKIRTING TYPE 2
SK.3	SKIRTING TYPE 3
	(GENERAL APARTMENT (REFER A.206 FOR TYPICAL DETAILS))
	(WET AREA TILED (REFER A.206 FOR TYPICAL DETAILS))
	(FOYER SKIRTING (REFER A.206 FOR TYPICAL DETAILS))

FOR CONSTRUCTION - 17/12/19